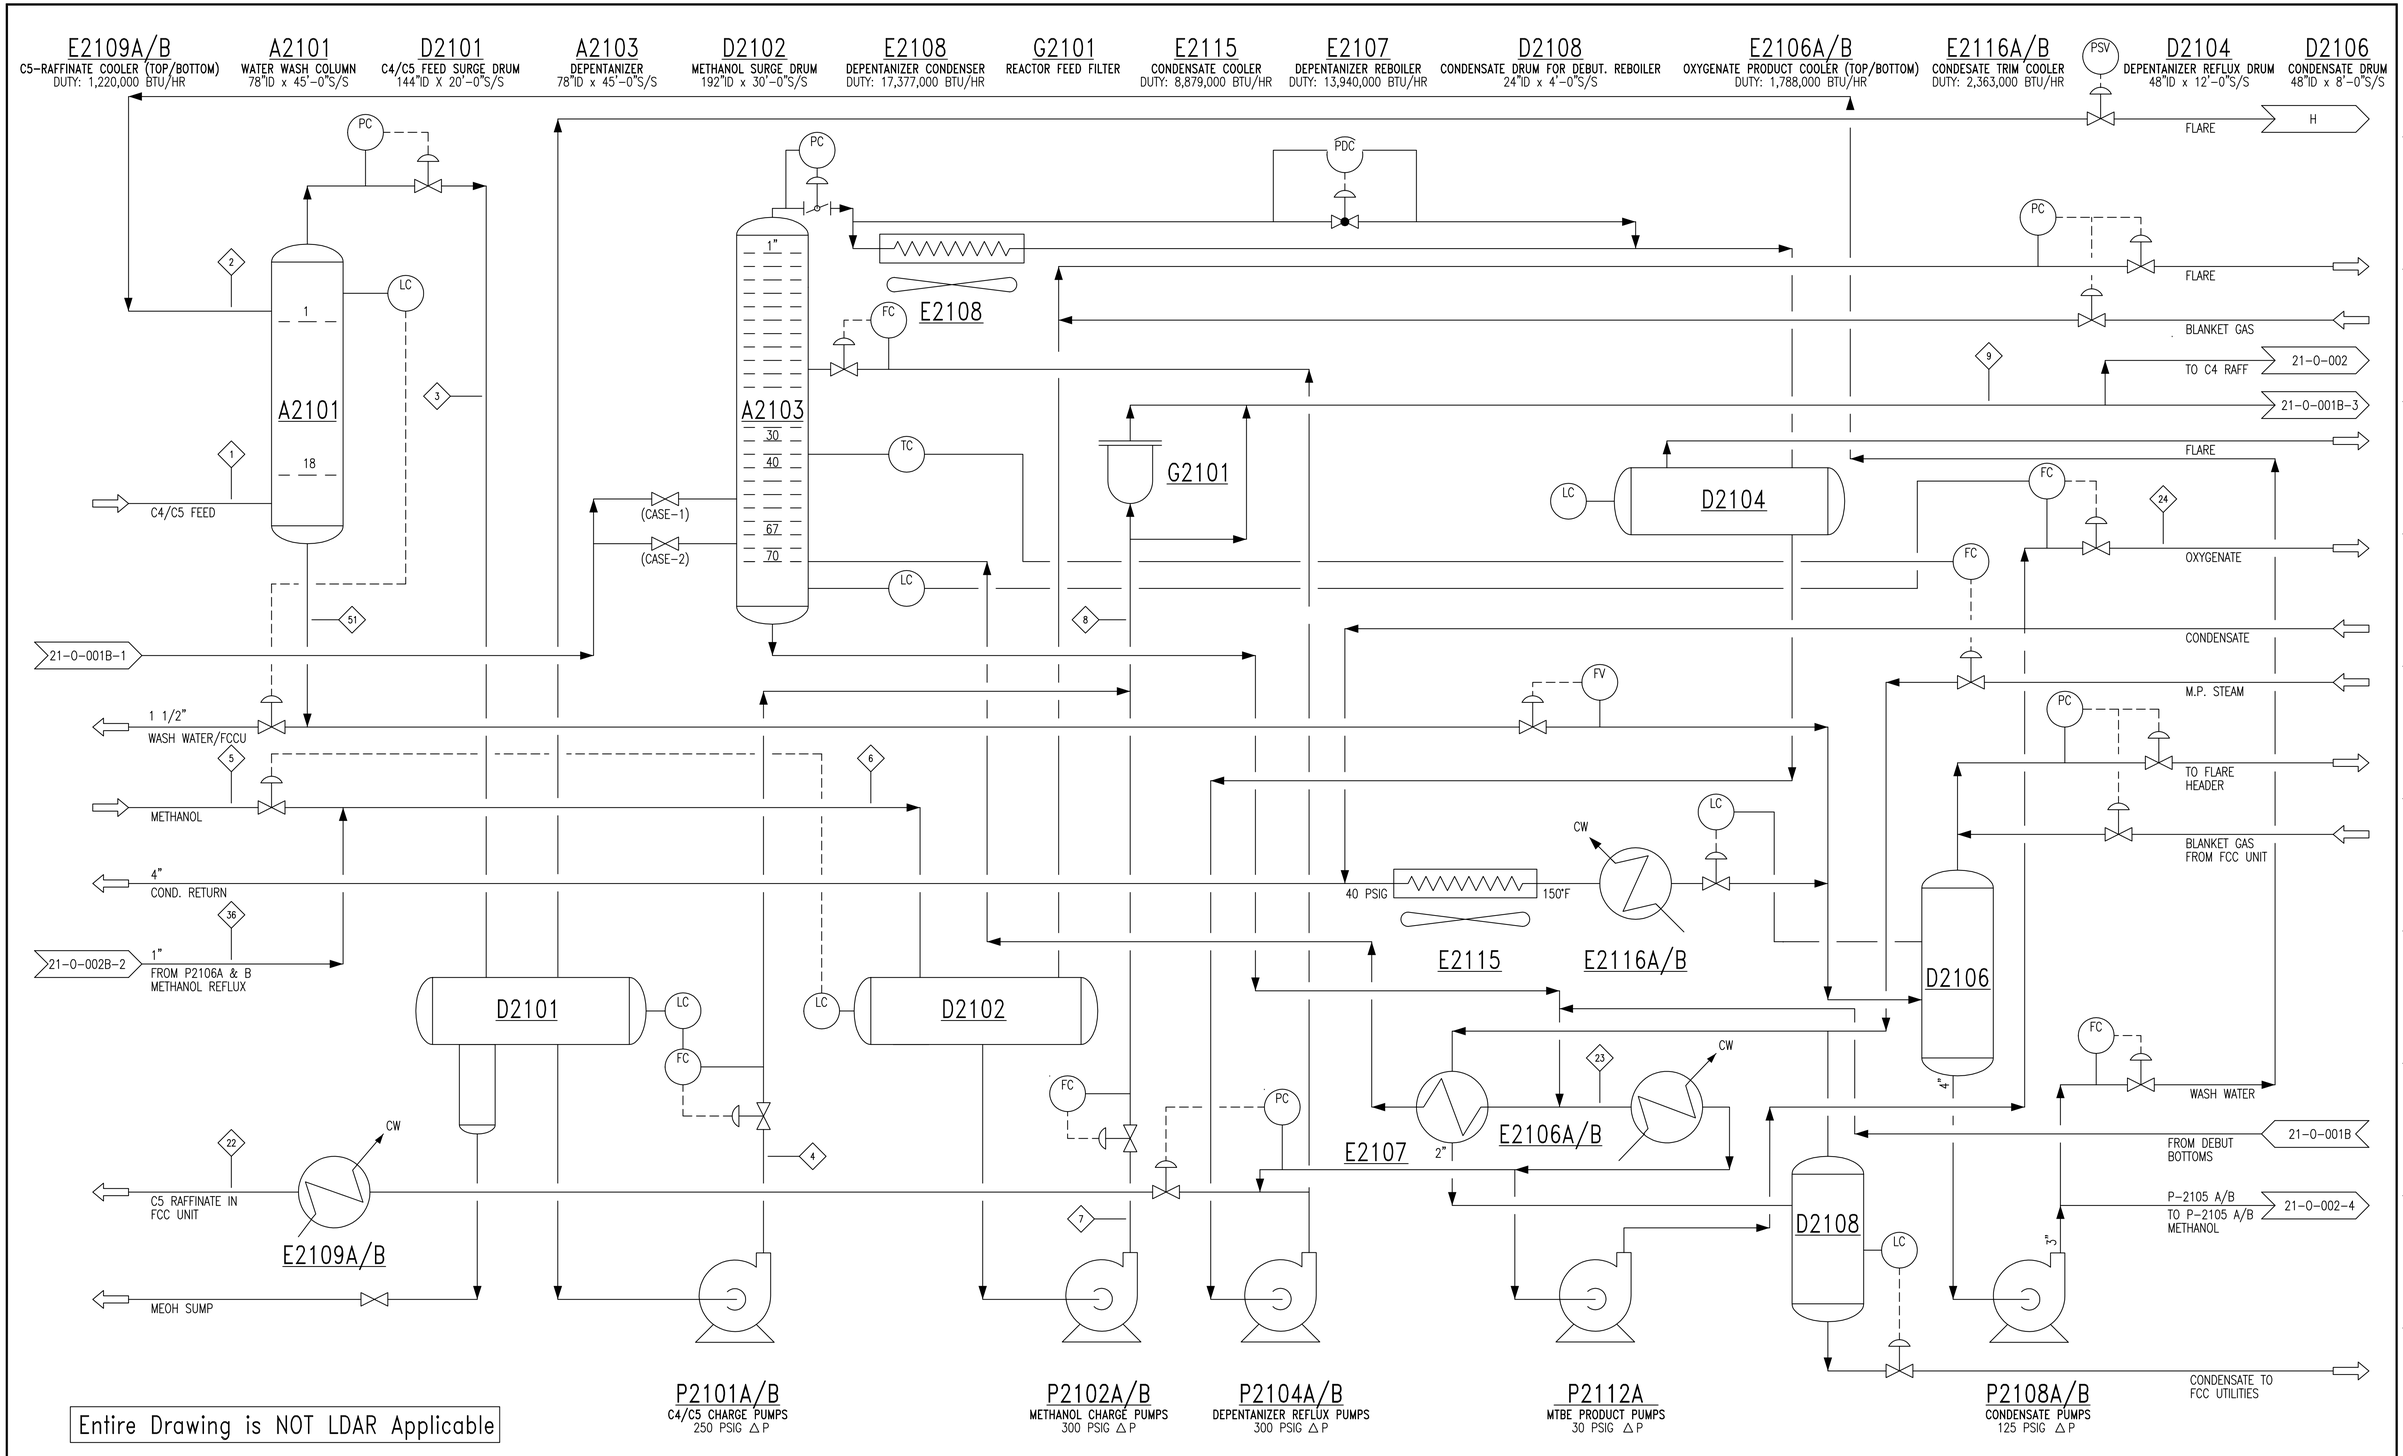

Entire Drawing is NOT LDAR Applicable

DWG. NO.	REFERENCE DRAWINGS	DWG. NO.	REFERENCE DRAWINGS
21-0-019	MATERIAL BALANCE		

NO.	REVISION	BY	CHK.	APP.	DATE	NO.	REVISION	BY	CHK.	APP.	DATE
1	UPDATED ON CAD FROM Howe-Baker DRAWING	RTS	RTS	TD	1-29-94						
2	UPDATED AS PER RFC 21-95-001	WHS	RTS	PHIBRO	8-21-95						
3	UPDATED AS PER RFC 21-02-017	HS	HS	VALERO	9-19-02						
4	UPDATED AS PER RFC 21-06-006	KJL	KJL	VALERO	3-29-06						

VALERO REFINING COMPANY - LOUISIANA

DWG. BY	CHK. BY	APP. BY	CAD FILE NAME
RDB	OPS	PHIBRO	21O001A

TITLE

PROCESS FLOW DIAGRAM
REACTION AND DEBUTANIZING
1800 BPSD MTBE UNIT

SCALE	DATE	UNIT	TYPE	JOB NO.	DWG. NO.	REV.
NTS	10-7-93	21			21-0-001A	4